


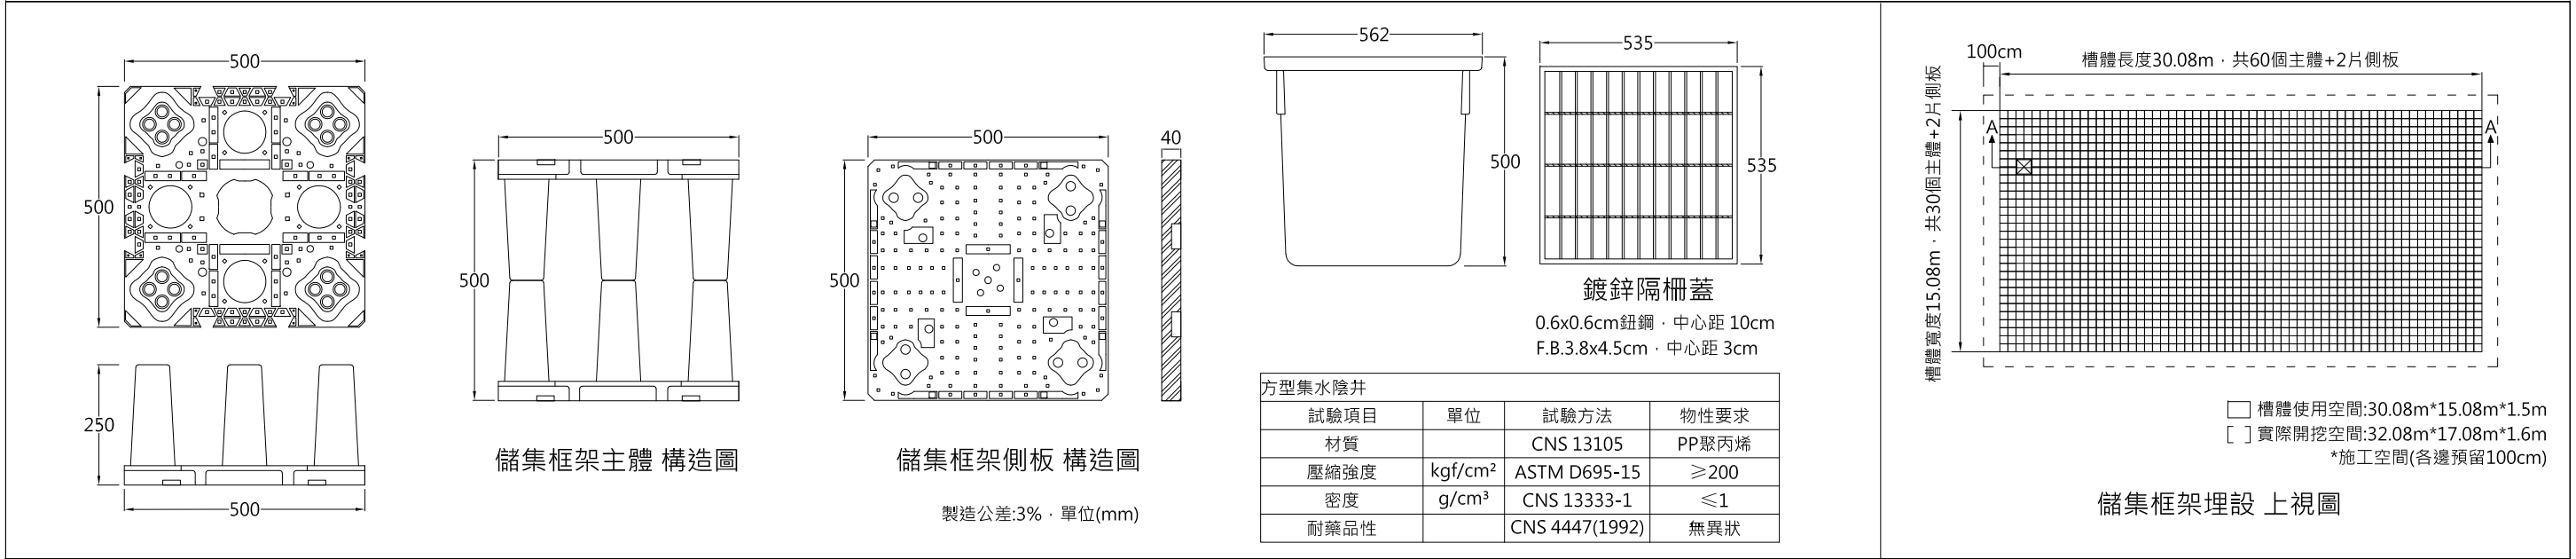

儲集框架材料規範

儲集框架主體				儲集框架側板			
試驗項目	單位	試驗方法	物性要求	試驗項目	單位	試驗方法	物性要求
材質		CNS 13105	聚丙烯	整體厚度	cm	游標卡尺	≥4
垂直極限抗壓強度	KN/m ²	CNS 2543	≥300	抗彎曲性能(抗壓)	mm	CNS 4392	≤1.8
產品本體重量	kg	電子計重秤	≥2.5	產品本體重量	kg	電子計重秤	≥2

*抗彎曲性能(抗壓):靜載重300kgf釋壓後變形量

透水不織布				防沉格網			
試驗項目	單位	試驗方法	物性要求	試驗項目	單位	試驗方法	物性要求
材質		CNS 13105	PP	材質		CNS 13105	PET
拉力強度(經緯向)	kgf	CNS 13483	≥200	表面保護層			SBR等環保樹脂
伸長率	%	CNS 13299	40~100	經緯雙向抗拉強度	KN/m	CNS 13300	≥100
梯形撕裂(經緯向)	kgf	CNS 13298	≥75	抗穿刺強度	N	ASTM D6241	≥11000
正向透水率	S ⁻¹	CNS 9024	≥0.8	網孔尺寸	mm	現場量測	4mm~9mm
耐紫外線性			外觀無變化				

*紫外線破弧燈連續照射200小時外觀無變化 · 抗拉力不得低於原規定之90%

儲集框架側板

HDPE不透水布

透水過濾布(保護層)

A1 細部詳圖

儲集框架主體

HDPE不透水布

透水過濾布(保護層)

A2 細部詳圖

儲集框架側板

HDPE不透水布

透水過濾布(保護層)

A3 細部詳圖

防沉格網


透水過濾布(保護層)

儲集框架主體

A4 細部詳圖

槽體範圍 30.08m*15.08m*1.5m	
使用面積(m ²)	453.61
儲水體積(m ³)	680.41
儲水率(%)	95
有效儲水容量(m ³)	646.39
儲集框架淨深(m)	1.5
上方覆土深度(m)	0.5~0.8
總埋設深度(m)	2~2.3

儲集框架 槽體概要表

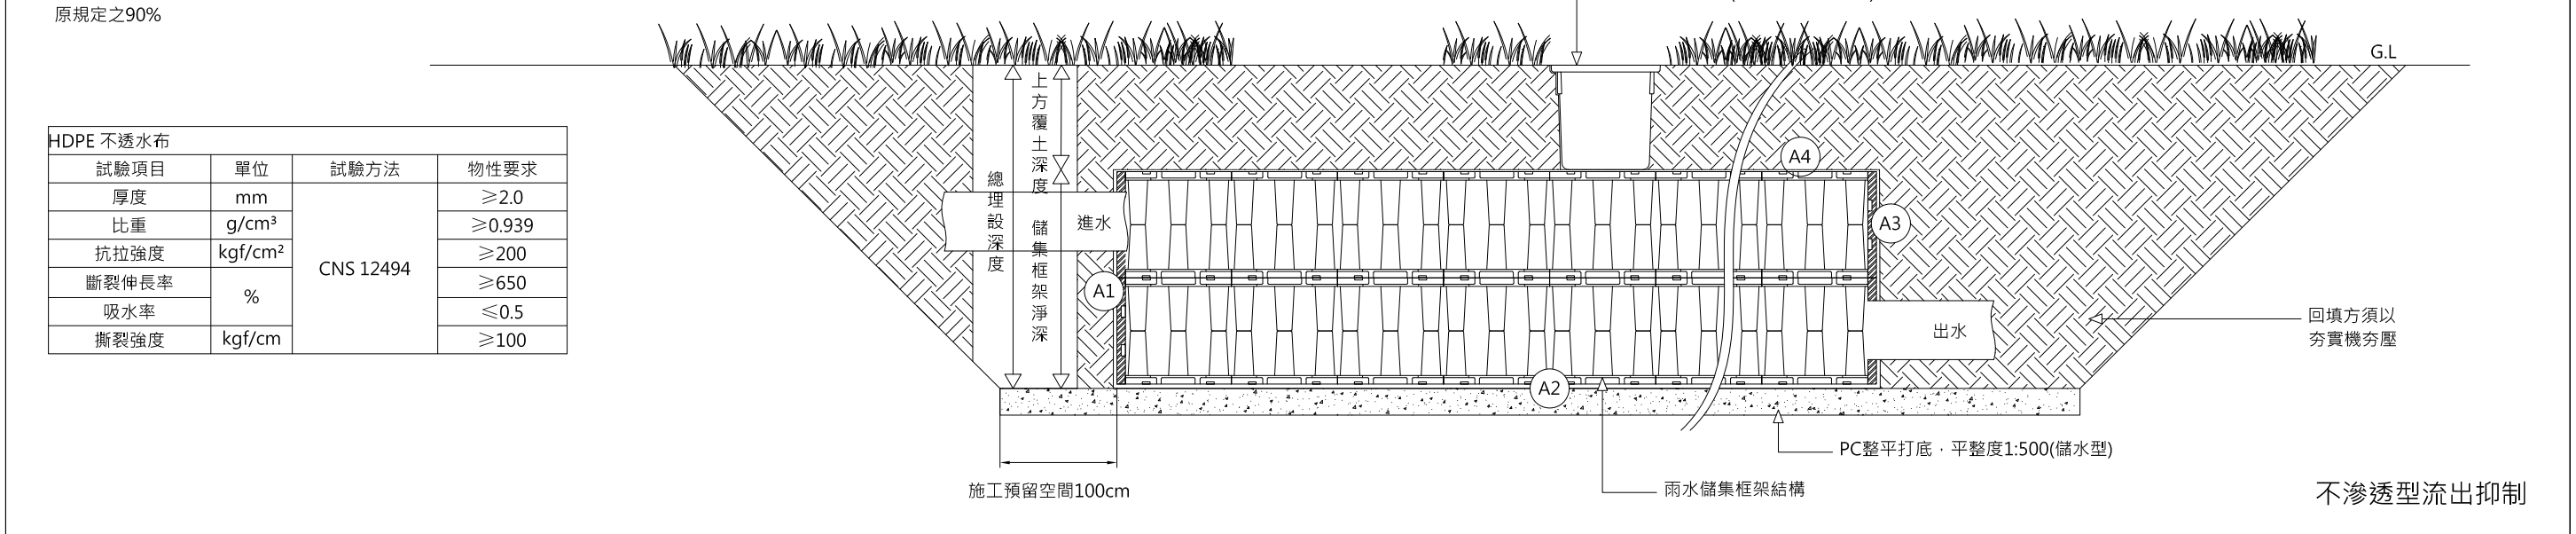

工程名稱	工程說明/修正記錄 NOTES & REVISION	 雨水管理大師 富勒創研有限公司 · 正在旺企業有限公司 台北市北投區清江路247巷8號1樓 Tel : (02)2898-6207 / Fax : (02)2898-6132 coinn@coinn.com.tw	業務號 JOB NO	繪圖 DRAWN	圖名 TITLE	圖號 DRAWING	專業簽證 SIGNATURE & SEALS	
	細部設計圖說		設計 DESIGNED	審核 CHECKED		張號 SHEET NO.		