

5000公升 地上型雨撲滿規範

一、槽體特性:

5噸容量地上型雨撲滿係以高密度聚乙稀(H.D.PE)為材質，槽體兩側有高抗壓補強肋，頂部上方設有兩處一體成形吊孔方便施工吊掛。

二、物性要求:


槽體以高密度聚乙烯製成，材質堅韌不易斷裂，物性要求如下：

地上型雨撲滿			
檢驗項目	單位	規定標準	測試標準
密度	g/cm ³	>0.935	CNS 13333-1
抗拉強度	kgf/cm ²	>180	CNS 15606-2
伸長率	%	>380	CNS 15606-2
抗衝擊強度	kJ/m ²	>40	CNS 13334

三、規格尺寸:

品名代號	儲水容量	雨撲滿尺寸(L*W*H)	人孔徑
SLT-5000	5000L	264*180*183(cm)	64cm



成品公差 ±3%

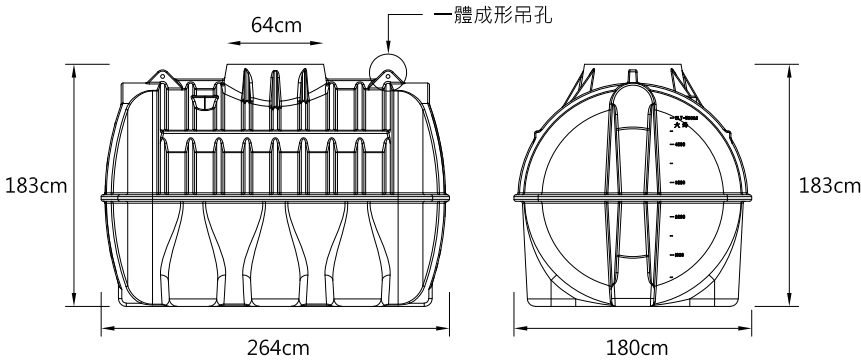


四、陰井蓋：

SMC陰井蓋採玻纖樹脂製成，內層以鋼條結構，外層包覆玻纖樹脂增加強度。

SMC陰井蓋尺寸			SMC陰井蓋-外框尺寸		
品名	外徑(mm)	厚度(mm)	品名	外徑(mm)	厚度(mm)
MH-700F	Ø700	30	MH-700F	Ø750	43

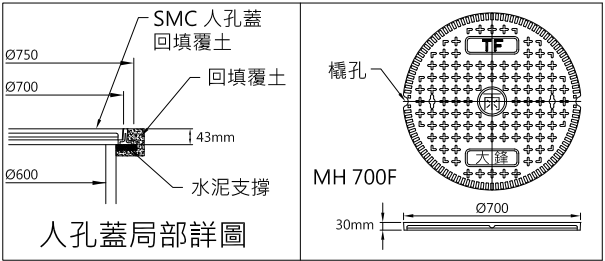
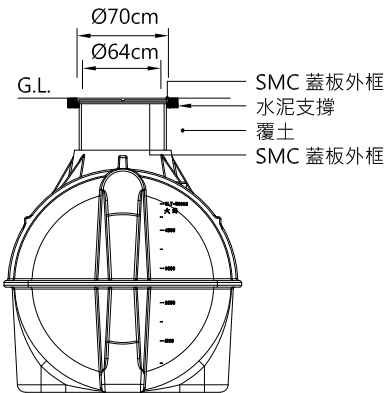


五、說明示意圖：

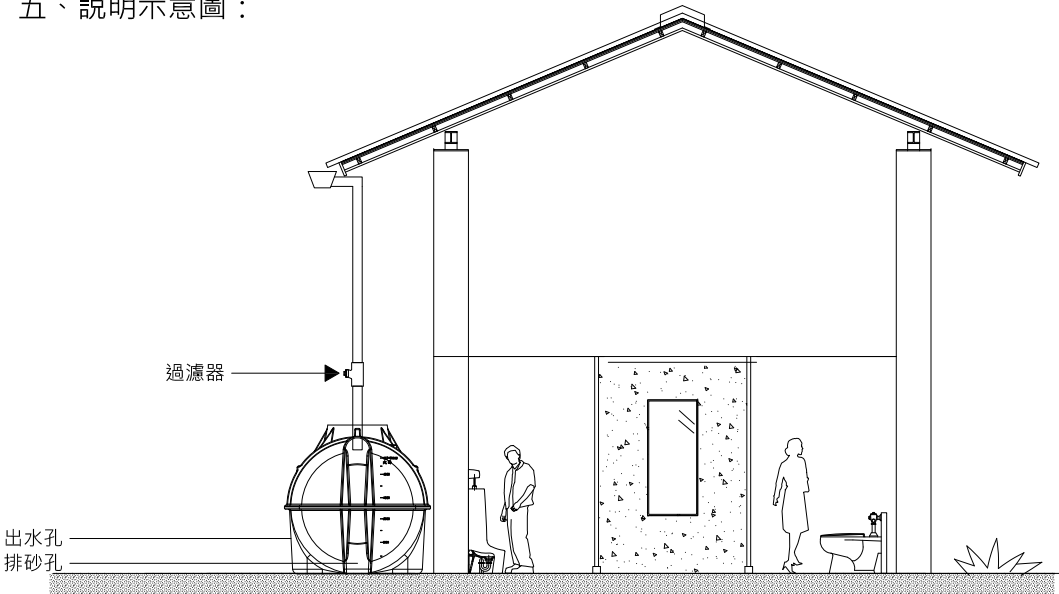

方型雨水過濾回收過濾系統示意圖

六、連結說明：

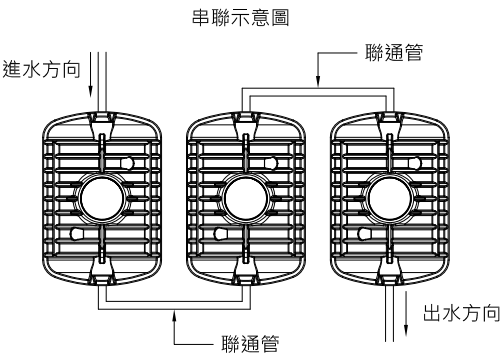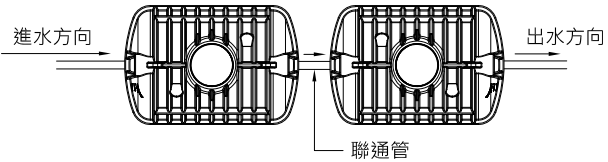

並聯示意圖

六、施工規範:

1. 雨撲滿放置前，基礎需先夯實，以確保地層穩定。
2. 雨撲滿依設計圖面所示放樣擺放，槽體之間依序配管接續。
3. 配管作業完成後，回填土至桶槽四分之一高度後先加以夯實槽體週邊土壤。
4. 儲槽上方如有車輛或重機械經過，人孔上方需加設保護鐵板。

工程名稱	工程說明/修正記錄 NOTES & REVISION	 雨水管理大師 高勤創研有限公司 • 正在旺企業有限公司 台北市北投區清江路247巷8號1樓 Tel : (02)2898-6207 / Fax : (02)2898-6132 coinn@coinn.com.tw	業務號 JOB NO	繪圖 DRAWN	圖名 TITLE	圖號 DRAWING	專業簽證 SIGNATURE & SEALS	
	細部設計圖說		設計 DESIGNED	審核 CHECKED		張號 SHEET NO.		