


≥60cm 深型花台排水 詳圖

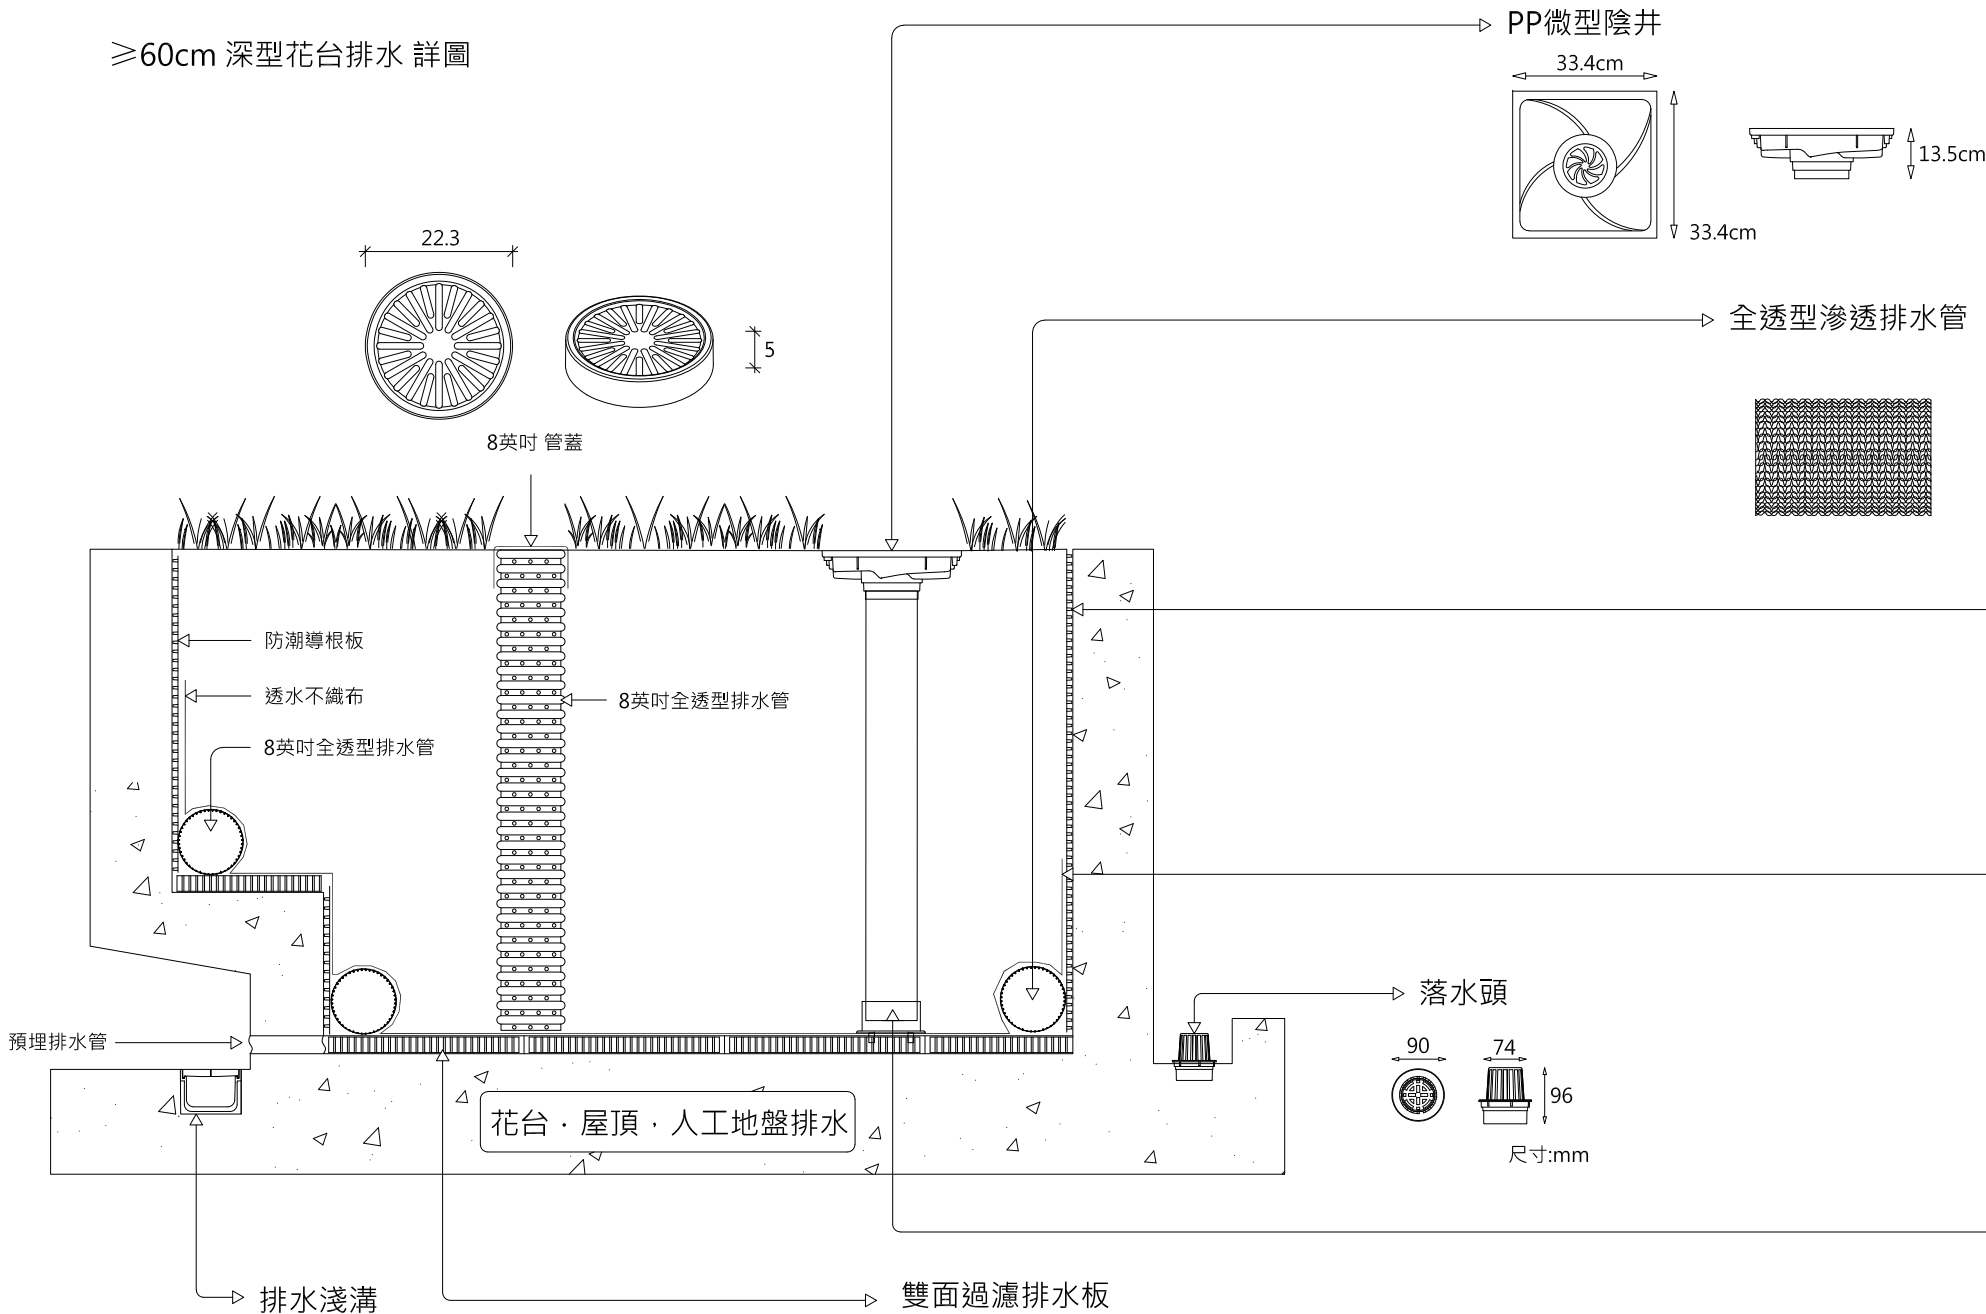

PP微型陰井(鑄鋁蓋)			
試驗項目	單位	試驗方法	要求值
衛氏軟化溫度	°C	ASTM D1525-17	≥90
抗拉強度	kgf/cm²	CNS 15606-3	≥220
抗壓強度		ASTM D695-15	≥250

滲透排水管			
試驗項目	單位	試驗方法	要求物性
灰分	%	CNS 2459	≤0.9
剛性	kgf/m²	CNS 14899	≥12000
抗拉強度	kgf/cm²	CNS 15606	≥265
伸長率	%		≥600
密度	g/cm³	CNS 13333-1	≥0.939

防潮阻根板


防潮阻根板			
試驗項目	單位	試驗方法	要求值
厚度	mm	CNS 4174	≥1.5
本體抗拉強度	kN/m	CNS 4396	≥35
接縫處抗拉強度			≥20
吸水率	%	CNS 3276	≤0.5

透水不織布

透水不織布			
試驗項目	單位	試驗方法	物性要求
材質		CNS 13105	PET
拉力強度(經緯向)	kgf	CNS 13483	≥60
伸長率	%		40~100
梯形撕裂(經緯向)	kgf	CNS 13299	≥25
正向透水率	S ⁻¹	CNS 13298	≥0.8
耐紫外線性		CNS 9024	外觀無變化

*紫外線破弧燈連續照射200小時外觀無變化，抗拉力不得低於原規定之90%


轉接頭腳座

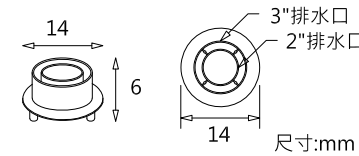

PP排水淺溝		
試驗項目	試驗方法	要求值
外徑寬度(cm)	量尺量測	12.5
外徑深度(cm)		8.5
拉力強度(kgf/cm²)	CNS 15606-3	≥150
伸長率(%)	CNS 15606-3	≥300

排水淺溝溝蓋		
試驗項目	試驗方法	要求值
溝面型式	目視	全平面・無弧度
防滑係數(長向)	CNS 8907	≥0.6
防滑係數(短向)		≥0.5

雙面過濾排水板

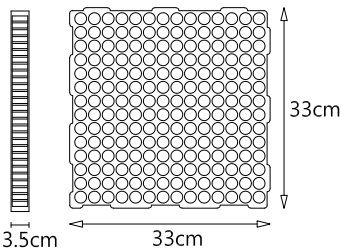

雙面過濾排水板			
試驗項目	單位	試驗方法	要求值
材質		CNS 13105	聚丙烯
抗壓強度	t/m²	ASTM D695-15	≥100
表面開孔面積	%	計算機	≥50
內部透空量體			≥85

工程名稱

工程說明/修正記錄
NOTES & REVISION

細部設計圖說



雨水管理大師

高勤創研有限公司・正在旺企業有限公司

台北市北投區清江路247巷8號1樓
Tel : (02)2898-6207 / Fax : (02)2898-6132
coinn@coinn.com.tw

業務號

JOB NO

設計

DESIGNED

繪圖

DRAWN

審核

CHECKED

圖名

TITLE

圖號

DRAWING

張號

SHEET NO.

專業簽證

SIGNATURE & SEALS