


斜屋頂排水設計

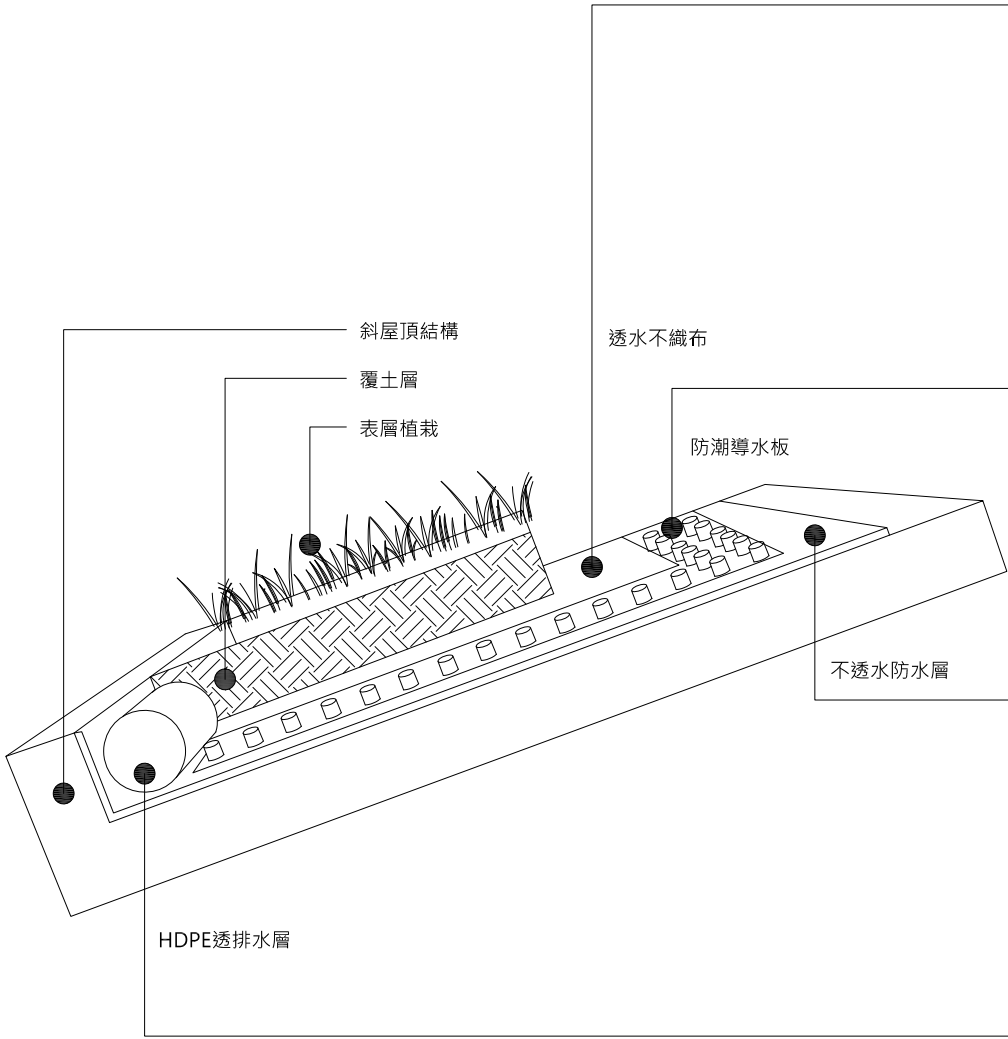

產品物性

透水不織布

試驗項目	單位	試驗方法	物性要求
材質		CNS 13105	PP
拉力強度(經緯向)	kgf	CNS 13483	≥200
伸長率	%		40~100
梯形撕裂(經緯向)	kgf	CNS 13299	≥75
正向透水率	S ⁻¹	CNS 13298	≥0.8
耐紫外線性		CNS 9024	外觀無變化

*紫外線破弧燈連續照射200小時外觀無變化，抗拉力不得低於原規定之90%

防潮導水板


試驗項目	單位	試驗方法	物性要求
材質		CNS 13105	HIPS
凸點高度	cm	卡尺量測	≥1

不透水防水層

試驗項目	單位	試驗方法	物性要求
厚度	mm	CNS 12494	≥2.0
比重	g/cm ³		≥0.939
抗拉強度	kgf/cm ²		≥200
斷裂伸長率	%		≥650
吸水率			≤0.5
撕裂強度	kgf/cm		≥100

HPDE滲透排水管

試驗項目	單位	試驗方法	要求物性
灰分	%	CNS 2459	≤0.9
剛性	kgf/m ²	CNS 14899	≥12000
抗拉強度	kgf/cm ²	CNS 15606	≥265
伸長率	%		≥600
密度	g/cm ³	CNS 13333-1	≥0.939

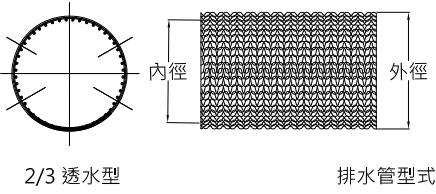

工程名稱	工程說明/修正記錄 NOTES & REVISION	 雨水管理大師 高勤創研有限公司 • 正在旺企業有限公司 台北市北投區清江路247巷8號1樓 Tel : (02)2898-6207 / Fax : (02)2898-6132 coinn@coinn.com.tw	業務號 JOB NO	繪圖 DRAWN	圖名 TITLE	圖號 DRAWING	專業簽證 SIGNATURE & SEALS	
	細部設計圖說		設計 DESIGNED	審核 CHECKED		張號 SHEET NO.		